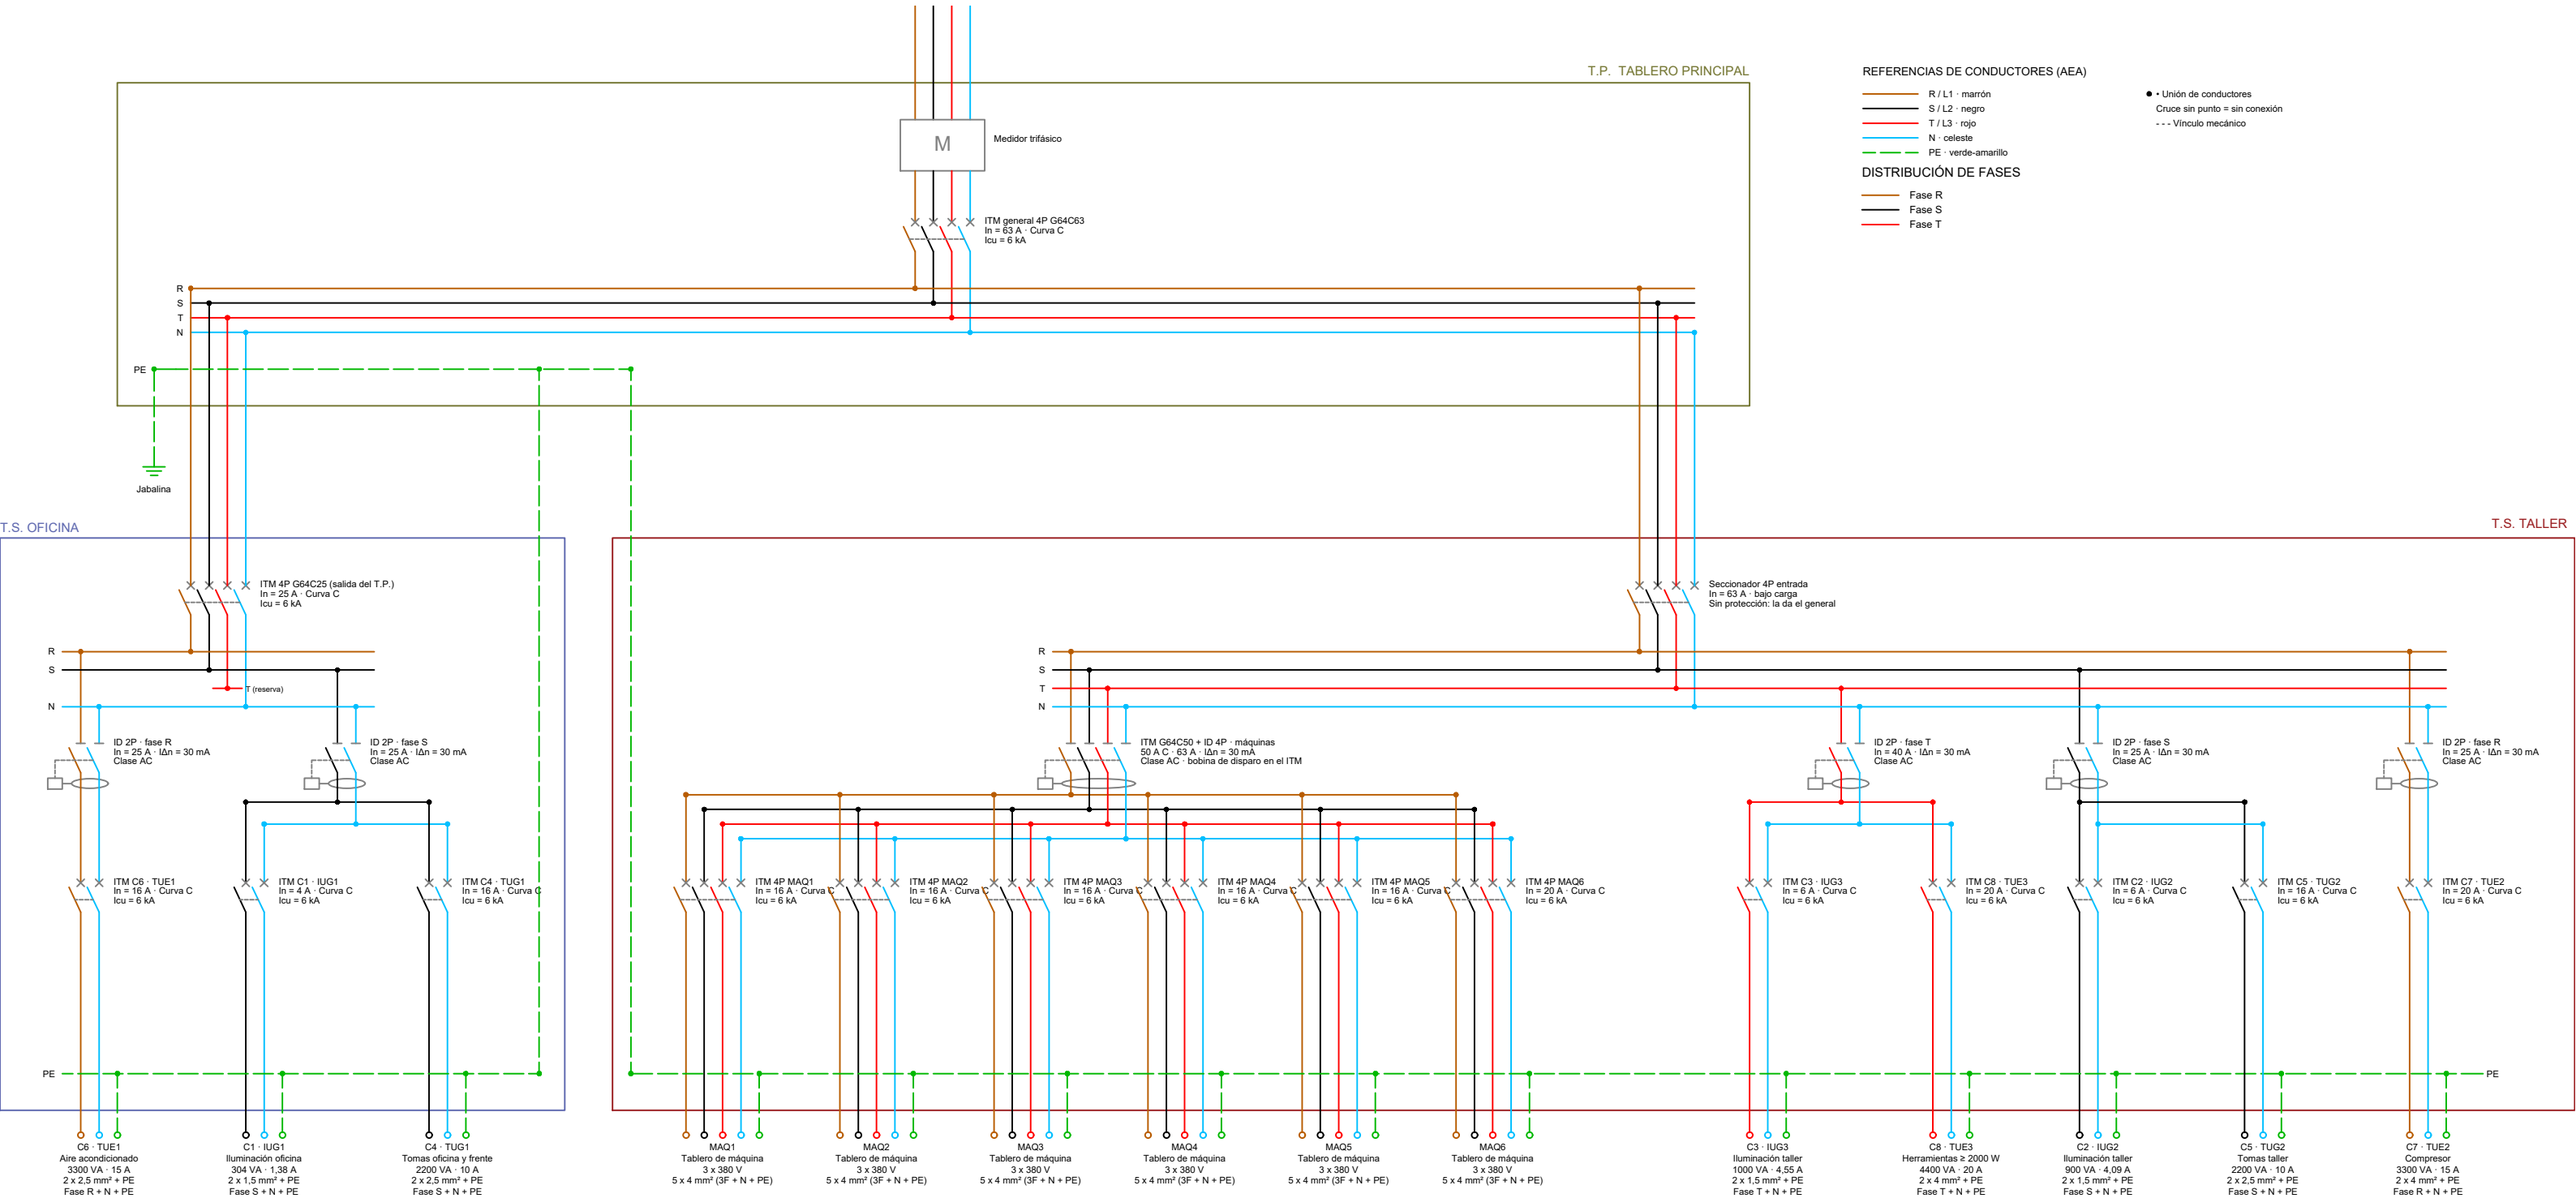

T.P. TABLERO PRINCIPAL
M
Medidor trifásico
ITM general 4P G64C63
In = 63 A · Curva C
Icu = 6 kA
R
S
T
N
PE
Jabalina
REFERENCIAS DE CONDUCTORES (AEA)
R / L1 · marrón
S / L2 · negro
T / L3 · rojo
N · celeste
PE · verde-amarillo
• Unión de conductores
Cruce sin punto = sin conexión
- - - Vínculo mecánico
DISTRIBUCIÓN DE FASES
Fase R
Fase S
Fase T
T.S. OFICINA
ITM 4P G64C25 (salida del T.P.)
In = 25 A · Curva C
Icu = 6 kA
T (reserva)
ID 2P · fase R
In = 25 A · IΔn = 30 mA
Clase AC
ID 2P · fase S
In = 25 A · IΔn = 30 mA
Clase AC
ITM C8 · TUE1
In = 16 A · Curva C
Icu = 6 kA
ITM C1 · IUG1
In = 4 A · Curva C
Icu = 6 kA
ITM C4 · TUG1
In = 16 A · Curva C
Icu = 6 kA
C6 · TUE1
Aire acondicionado
3300 VA · 15 A
2 x 2,5 mm² + PE
Fase R + N + PE
C1 · IUG1
Iluminación oficina
304 VA · 1,38 A
2 x 1,5 mm² + PE
Fase S + N + PE
C4 · TUG1
Tomas oficina y frente
2200 VA · 10 A
2 x 2,5 mm² + PE
Fase S + N + PE
T.S. TALLER
Seccionador 4P entrada
In = 63 A · bajo carga
Sin protección: la da el general
ITM G64C50 + ID 4P · máquinas
50 A C · 63 A · IΔn = 30 mA
Clase AC · bobina de disparo en el ITM
ITM 4P MAQ1
In = 16 A · Curva C
Icu = 6 kA
ITM 4P MAQ2
In = 16 A · Curva C
Icu = 6 kA
ITM 4P MAQ3
In = 16 A · Curva C
Icu = 6 kA
ITM 4P MAQ4
In = 16 A · Curva C
Icu = 6 kA
ITM 4P MAQ5
In = 16 A · Curva C
Icu = 6 kA
ITM 4P MAQ6
In = 20 A · Curva C
Icu = 6 kA
MAQ1
Tablero de máquina
3 x 380 V
5 x 4 mm² (3F + N + PE)
MAQ2
Tablero de máquina
3 x 380 V
5 x 4 mm² (3F + N + PE)
MAQ3
Tablero de máquina
3 x 380 V
5 x 4 mm² (3F + N + PE)
MAQ4
Tablero de máquina
3 x 380 V
5 x 4 mm² (3F + N + PE)
MAQ5
Tablero de máquina
3 x 380 V
5 x 4 mm² (3F + N + PE)
MAQ6
Tablero de máquina
3 x 380 V
5 x 4 mm² (3F + N + PE)
ID 2P · fase T
In = 40 A · IΔn = 30 mA
Clase AC
ITM C3 · IUG3
In = 6 A · Curva C
Icu = 6 kA
C3 · IUG3
Iluminación taller
1000 VA · 4,55 A
2 x 1,5 mm² + PE
Fase T + N + PE
ITM C8 · TUE3
In = 20 A · Curva C
Icu = 6 kA
C8 · TUE3
Herramientas ≥ 2000 W
4400 VA · 20 A
2 x 4 mm² + PE
Fase T + N + PE
ID 2P · fase S
In = 25 A · IΔn = 30 mA
Clase AC
ITM C2 · IUG2
In = 6 A · Curva C
Icu = 6 kA
C2 · IUG2
Iluminación taller
900 VA · 4,09 A
2 x 1,5 mm² + PE
Fase S + N + PE
ITM C5 · TUG2
In = 16 A · Curva C
Icu = 6 kA
C5 · TUG2
Tomas taller
2200 VA · 10 A
2 x 2,5 mm² + PE
Fase S + N + PE
ID 2P · fase R
In = 25 A · IΔn = 30 mA
Clase AC
ITM C7 · TUE2
In = 20 A · Curva C
Icu = 6 kA
C7 · TUE2
Compresor
3300 VA · 15 A
2 x 4 mm² + PE
Fase R + N + PE